

※ 본 도면은 소프트웨어 시험용으로 만든 가상 도면이며 실제 건축물이 아님

건 축 개 요

구 분	내 용
공사명	가상동 근린생활시설 신축공사 (시험용 가상 도면)
대지위치	경기도 용인시 수지구 가상동 123-4
지역·지구	제2종일반주거지역, 가로구역별 최고높이 미지정
주용도	제2종 근린생활시설(사무소)
대지면적	330.00 ㎡
건축면적	205.00 ㎡
건폐율	62.12 % (법정 60% 이하)
연면적	940.00 ㎡ (지하 120.00 ㎡ / 지상 820.00 ㎡)
용적률 산정용 연면적	820.00 ㎡
용적률	248.48 % (법정 240% 이하)
규모	지하 1층, 지상 4층
최고높이	14.2 m
구조	철근콘크리트조
주차대수	3 대 (1층 필로티 자주식)
조경면적	12.00 ㎡
전면도로	남측 6.0 m 도로, 접도길이 1.8 m
정북방향 이격	높이 10m 이하 부분 1.5 m / 10m 초과 부분 6.0 m

도 면 목 록

도면번호	도면명
A-001	건축개요 및 도면목록
A-002	면적표
A-101	배치도
A-201	입면도

건축사
(인)

공 사 명	가상동 근린생활시설 신축공사 (시험용 가상 도면)
설 계 자	가상건축사사무소 (시험용)
도 면 명	건축개요 및 도면목록
도면번호	A-001
축 척	NONE
일 자	2026. 09.

※ 본 도면은 소프트웨어 시험용으로 만든 가상 도면이며 실제 건축물이 아님

층 별 면 적 표

층	용도	바닥면적(㎡)	용적률 산정
지하1층	기계실·창고	120.00	제외
1층	제2종 근린생활시설(사무소)	205.00	산입
2층	제2종 근린생활시설(사무소)	205.00	산입
3층	제2종 근린생활시설(사무소)	205.00	산입
4층	제2종 근린생활시설(사무소)	205.00	산입
합계		940.00	820.00

건축사
(인)

공 사 명	가상동 근린생활시설 신축공사 (시험용 가상 도면)
설 계 자	가상건축사사무소 (시험용)
도 면 명	면적표
도면번호	A-002
축 척	NONE
일 자	2026. 09.

※ 본 도면은 소프트웨어 시험용으로 만든 가상 도면이며 실제 건축물이 아님



대지경계선 (대지면적 330.00㎡)

※ 높이 10m 초과 부분 경복 이격 6.0 m (단면도 참조)

경복 이격 1.5 m
(높이 10m 이하)

계획 건축물
건축면적 205.00㎡
지상4층 / 지하1층

1층 필로티 하부 주차

P1

P2

P3

조경
12.00㎡

건축사
(인)

접도길이 1.8 m


6.0 m 도로

주차 계획: 1층 필로티 자주식 3대 (2.3m×5.0m)

공 사 명	가상동 근린생활시설 신축공사 (시험용 가상 도면)
설 계 자	가상건축사사무소 (시험용)
도 면 명	배치도
도면번호	A-101
축 척	1/100
일 자	2026. 09.

※ 본 도면은 소프트웨어 시험용으로 만든 가상 도면이며 실제 건축물이 아님

정 면 도 (남측)

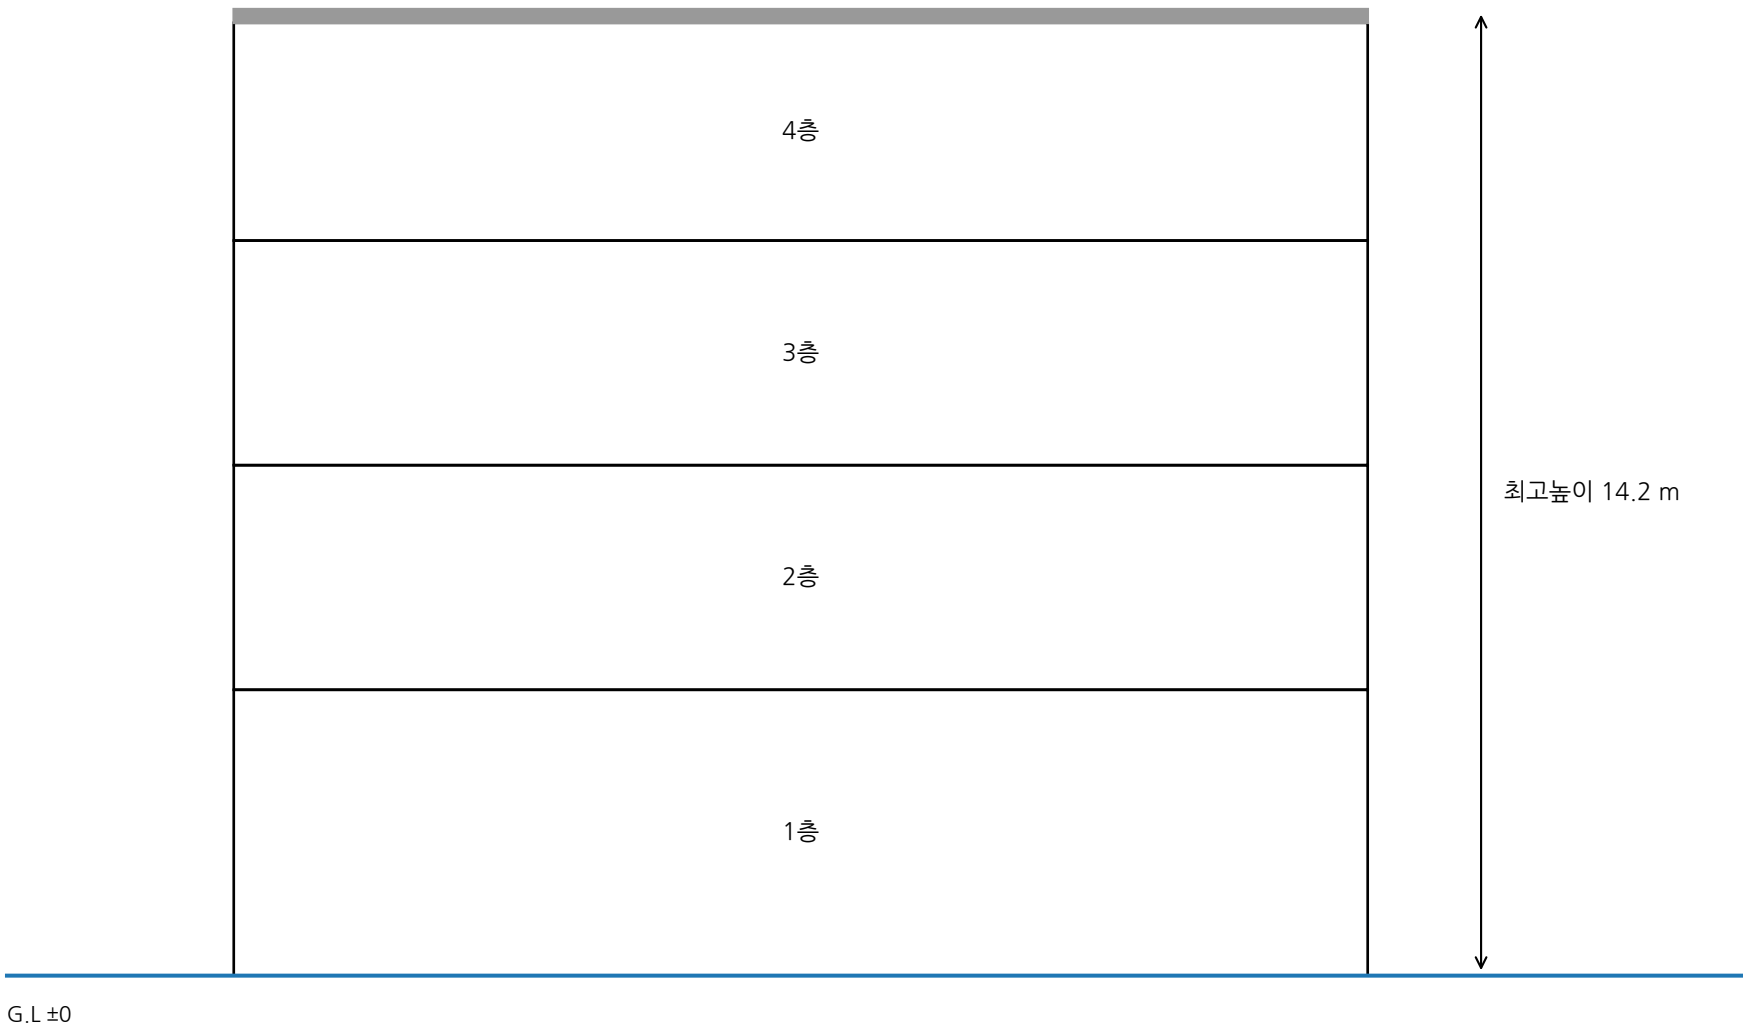

건축사
(인)

공 사 명	가상동 근린생활시설 신축공사 (시험용 가상 도면)
설 계 자	가상건축사사무소 (시험용)
도 면 명	입면도
도면번호	A-201
축 척	1/100
일 자	2026. 09.